

Room Layout Sheet

Room Name

RDS Room Code 1 BR-LG-28-I

BFG	BAR FRIDGE
BLK	BEDSIDE LOCKER
BPT	BODY PROTECTED
BSC	BED SCREEN CURTAIN
BSCT	BED SCREEN CURTAIN TRACK
BSN	BASSINET
CG	CORNER GUARD
CHP	CHAIR - PATIENT
CHV	CHAIR - VISITOR
COM/2	COMMUNICATION OUTLET - DOUBLE
DDG	DISPENSER - DISPOSABLE GLOVES
DFP	DOOR AND DOOR FRAME PROTECTION
DHT	DISPENSER - HAND TOWEL
DK-TVU	DESK AND TV UNIT
DMS	DISPENSER - MOISTURISER
DS	DISPENSER - SOAP
DSA	DISPENSER - SOAP ANTISEPTIC
EC	EMERGENCY CALL
GPO/1	GENERAL POWER OUTLET - SINGLE
GPO/1EP	EMERGENCY POWER OUTLET - SINGLE
GPO/2	GENERAL POWER OUTLET - DOUBLE
GPO/C	GENERAL POWER OUTLET - CLEANER'S
HW-B	HAND WASH BASIN, TYPE'B'
IEB	INPATIENT ELECTRIC BED
LS/B	LIGHT SWITCH - BED
LS/E	LIGHT SWITCH - ENSUITE
LS/R	LIGHT SWITCH - ROOM
LS/RL	LIGHT SWITCH - READING LIGHT
MA	MEDICAL AIR
MATV	MASTER ANTENNA TV
O2	OXYGEN
PB/F	PIN BOARD, FABRIC COVERED
PCH	PATIENT CALL HANDSET
PS	PATIENT TO STAFF CALL
RBH	ROLLER BLIND: HOLLAND
S	SUCTION
SA	STAFF ASSIST CALL
SBB	SUCTION BOTTLE BRACKET
SBK	SPLASHBACK
ST	SENSOR TAP
TEL	TELEPHONE
TOB	TABLE: OVERBED
TV	TELEVISION SET
WBM	WHITE BOARD - MAGNETIC
WBP	WASTE BIN, PAPER
WPP	WALL PROTECTION PANEL
WRD-BFC-FSH	WARDROBE & BAR FRIDGE CUPBOARD WITH FLOWER SHELF
PBB	PLASTERBOARD BULKHEAD, PAINT FINISH
V1	VINYL FLOORING, STANDARD SLIP RESISTANT
V6	VINYL FLOORING, NON-SLIP TEXTURED
SK4	FLOOR VINYL COVED SKIRTING
WPF	WALL PAINT FINISH



This document is for advisory purpose only

iHFG Standard Components


Room Layout Sheet

Room Name 1 Bed Room - Large, 28m²


RLS Room Code 1 BR-LG-28B-I
RDS Room Code 1 BR-LG-28-I

Abbreviations


BFG	BAR FRIDGE
BLK	BEDSIDE LOCKER
BPT	BODY PROTECTED
BSC	BED SCREEN CURTAIN
BSCT	BED SCREEN CURTAIN TRACK
BSN	BASSINET
CG	CORNER GUARD
CHP	CHAIR – PATIENT
CHV	CHAIR – VISITOR
COM/2	COMMUNICATION OUTLET – DOUBLE
DDG	DISPENSER – DISPOSABLE GLOVES
DFP	DOOR AND DOOR FRAME PROTECTION
DHT	DISPENSER – HAND TOWEL
DK-TVU	DESK AND TV UNIT
DMS	DISPENSER – MOISTURISER
DS	DISPENSER – SOAP
DSA	DISPENSER – SOAP ANTISEPTIC
EC	EMERGENCY CALL
GPO/1	GENERAL POWER OUTLET – SINGLE
GPO/1EP	EMERGENCY POWER OUTLET – SINGLE
GPO/2	GENERAL POWER OUTLET – DOUBLE
GPO/C	GENERAL POWER OUTLET – CLEANER'S
HW-B	HAND WASH BASIN, TYPE'B'
IEB	INPATIENT ELECTRIC BED
LS/B	LIGHT SWITCH – BED
LS/E	LIGHT SWITCH – ENSUITE
LS/R	LIGHT SWITCH – ROOM
LS/RL	LIGHT SWITCH – READING LIGHT
MA	MEDICAL AIR
MATV	MASTER ANTENNA TV
O2	OXYGEN
PB/F	PIN BOARD, FABRIC COVERED
PCH	PATIENT CALL HANDSET
PS	PATIENT TO STAFF CALL
RBH	ROLLER BLIND: HOLLAND
S	SUCTION
SA	STAFF ASSIST CALL
SBB	SUCTION BOTTLE BRACKET
SBK	SPLASHBACK
ST	SENSOR TAP
TEL	TELEPHONE
TOB	TABLE: OVERBED
TV	TELEVISION SET
WBM	WHITE BOARD – MAGNETIC
WBP	WASTE BIN, PAPER
WPP	WALL PROTECTION PANEL
WRD-BFC-FSH	WARDROBE & BAR FRIDGE CUPBOARD WITH FLOWER SHELF
PBB	PLASTERBOARD BULKHEAD, PAINT FINISH
SK4	FLOOR VINYL COVERED SKIRTING
WPF	WALL PAINT FINISH
V1	VINYL FLOORING, STANDARD SLIP RESISTANT
V6	VINYL FLOORING, NON-SLIP TEXTURED

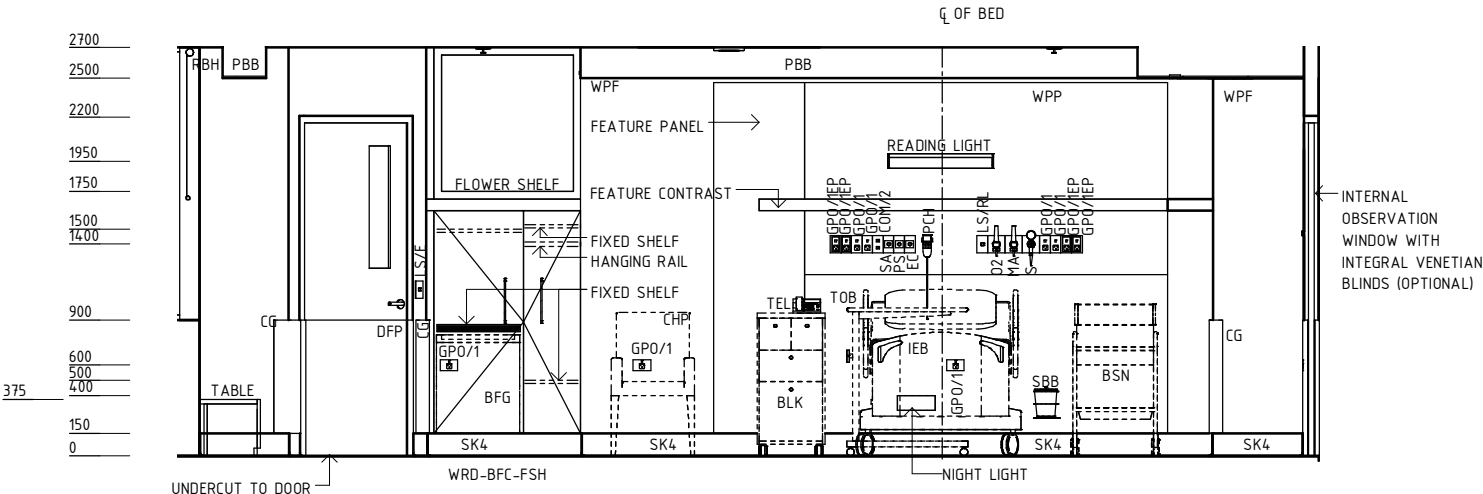

ELEVATION 2

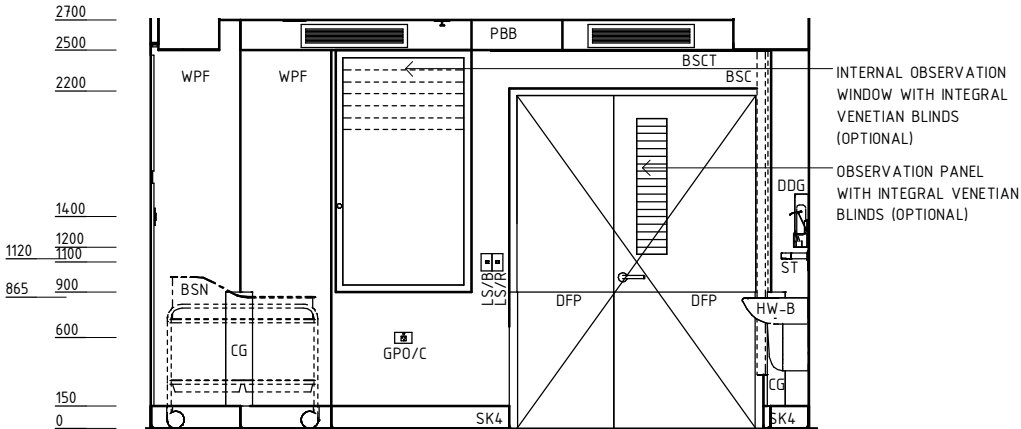

ELEVATION 3

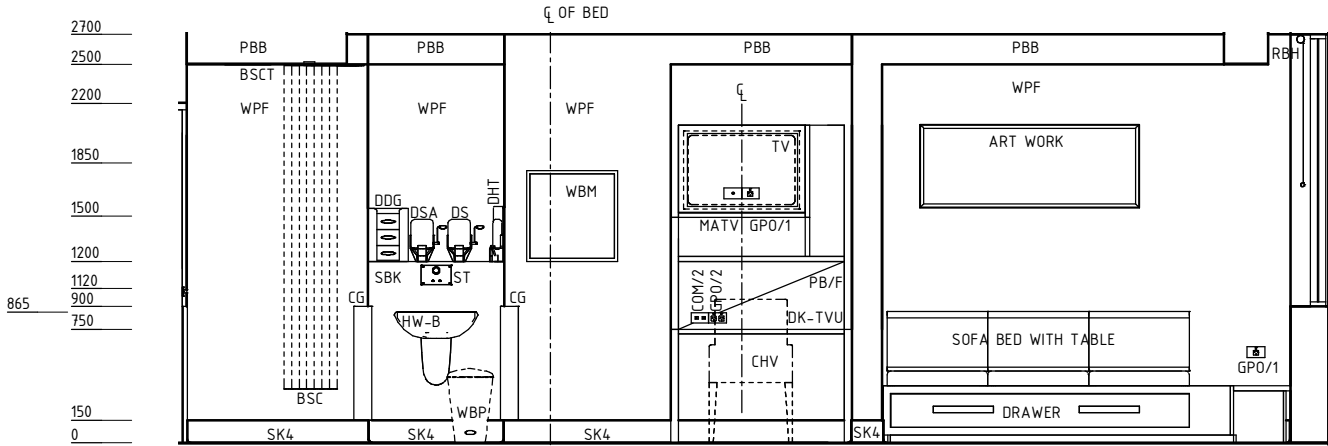

ELEVATION 4

REV	DESCRIPTION	DATE	BY	REV	DESCRIPTION	DATE	BY	REV	DESCRIPTION	DATE	BY
1	FIRST REVISION	22.02.2013	CT								
2	SECOND REVISION	30.05.2013	NB								

iHFG

International Health Facility Guidelines

International Health Facility Guidelines at:
www.healthdesign.com.au/iHFG
Editable version of Standard Components on
Health Facility Briefing System (HFBS) at:
www.healthdesign.com.au
©TAHPI

DESIGNED	APPROVED	DATE	SCALE(S)	SHEET
RC/ CT	DB	18/10/12	1 : 50	2 of 5
REVIT FILE NAME	PAPER DRAWING ID	ISSUE		
1 BR-LG-28B-I	1 BR-LG-28B-Ib	1		

This document is for advisory purpose only

Room Layout Sheet

RLS Room Code 1 BR-LG-28B-I
RDS Room Code 1 BR-LG-28-I

THIS DRAWING TO BE READ IN CONJUNCTION WITH R.D.S.
(ROOM DATA SHEETS) WHICH TAKES PRECEDENCE.

ALL SERVICES INDICATED ARE INDICATIVE AND SUBJECTED TO DETAILED PROJECT SPECIFIC ENGINEERING DESIGN.

Diagram illustrating a ceiling type cornice. The cornice is labeled BP-PC2 and has a height of 2700. The height is measured above the finished floor level (F.F.L.). The diagram also indicates the ceiling type and cornice type.

PB-PC4	PLASTERBOARD FLUSH SET CEILING, PAINT FINISH WITH POWDERCOAT ALUMINIUM CORNICE, SHADOW ANGLE 24mm
PBB	PLASTERBOARD BULKHEAD, PAINT FINISH


— — — — — GRID LINE

ELECTRICAL LEGEND:

	DL	DOWNLIGHT - RECESSED
	DL-DIR	DIRECTIONAL DOWNLIGHT - RECESSED
	DLF-C	FLUORESCENT DIFFUSED DOWNLIGHT - RECESSED, COLOUR CORRECTED
	SL	CONTINUOUS STRIP LIGHT - RECESSED

	SUPPLY AIR GRILLE
	SUPPLY AIR GRILLE
	RETURN AIR OR TRANSFER GRILLE

	SMOKE DETECTOR
	SPRINKLER

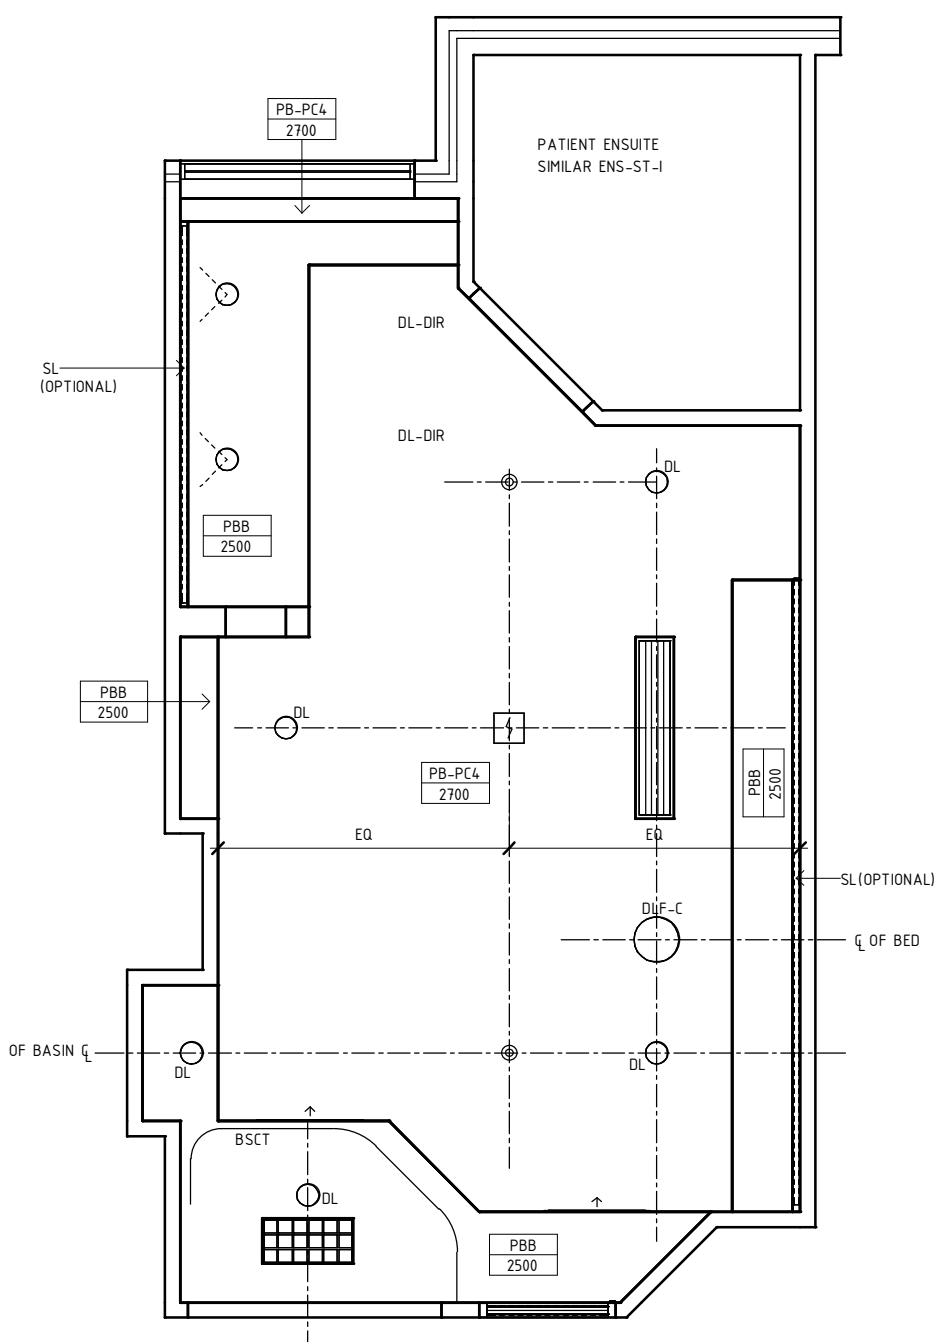

REFLECTED CEILING PLAN

REV	DESCRIPTION	DATE	BY	REV	DESCRIPTION	DATE	BY	REV	DESCRIPTION	DATE	BY
1	FIRST REVISION	22.02.2013	CT								
2	SECOND REVISION	30.05.2013	NB								



International Health Facility Guidelines at:
www.healthdesign.com.au/iHFG
 Editable version of Standard Components on
 Health Facility Briefing System (HFBS) at:
www.healthdesign.com.au
 ©TAHPI

DESIGNED	APPROVED	DATE	SCALE(S)	SHEET
RC/ CT/ NB	DB	18/10/12	1 : 50	3 of 5
REVIT FILE NAME 1 BR-LG-28B-I		PAPER DRAWING ID 1 BR-LG-28B-Ic		ISSUE 1


iHFG Standard Components

Room Layout Sheet


Room Name 1 Bed Room - Large, 28m²

RLS Room Code 1 BR-LG-28B-I
RDS Room Code 1 BR-LG-28-I


Abbreviations

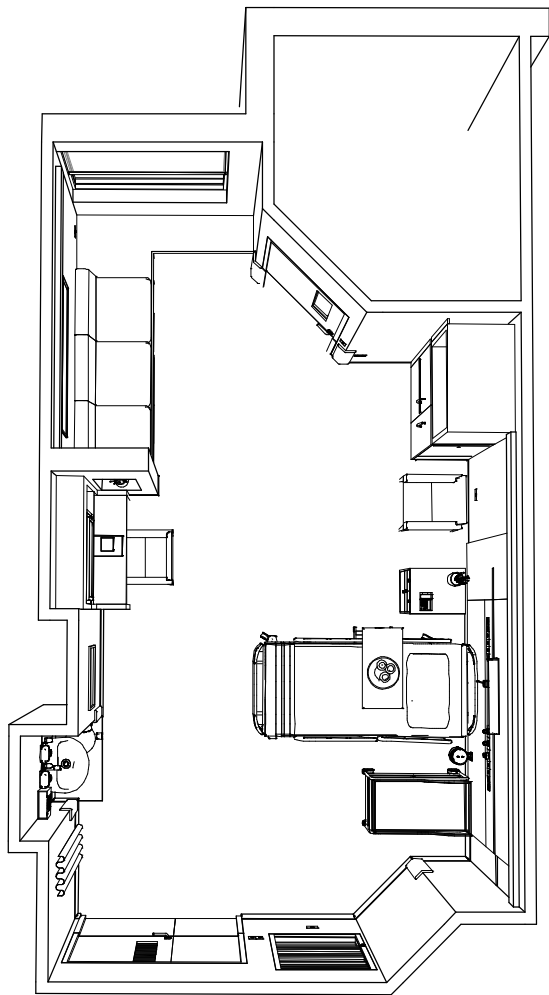

PERSPECTIVE PLAN VIEW

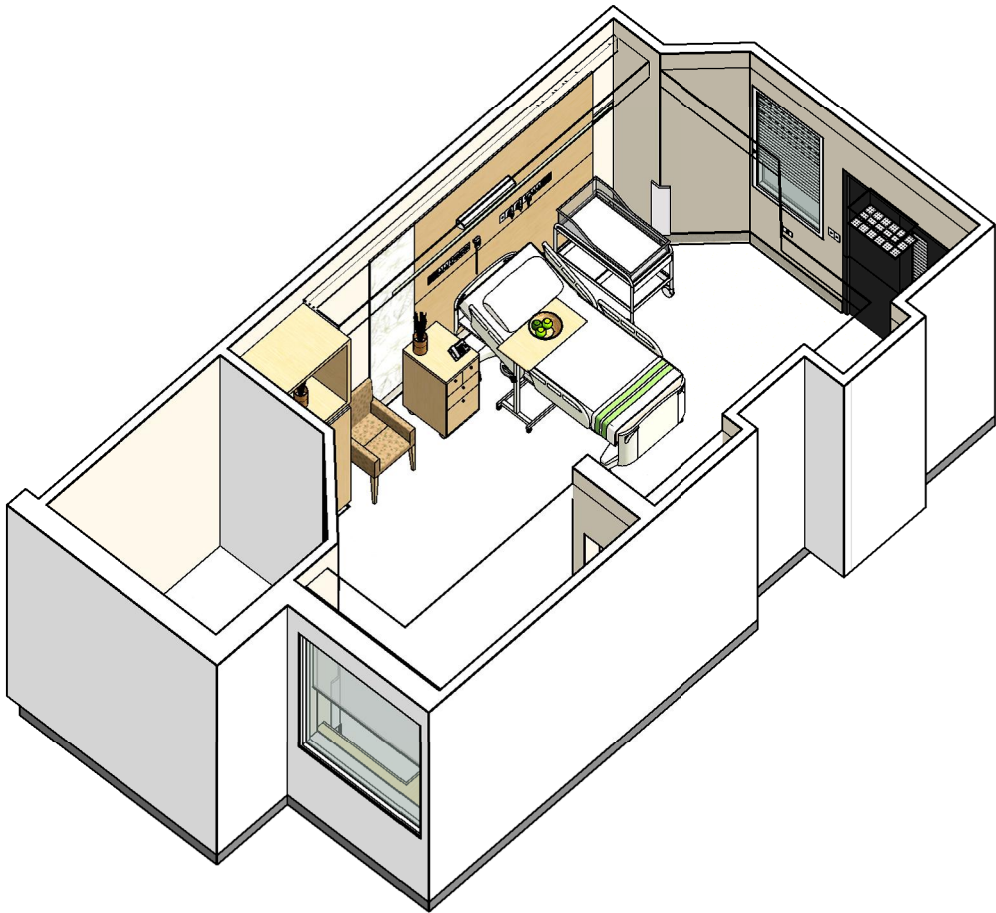

ISOMETRIC VIEW 01

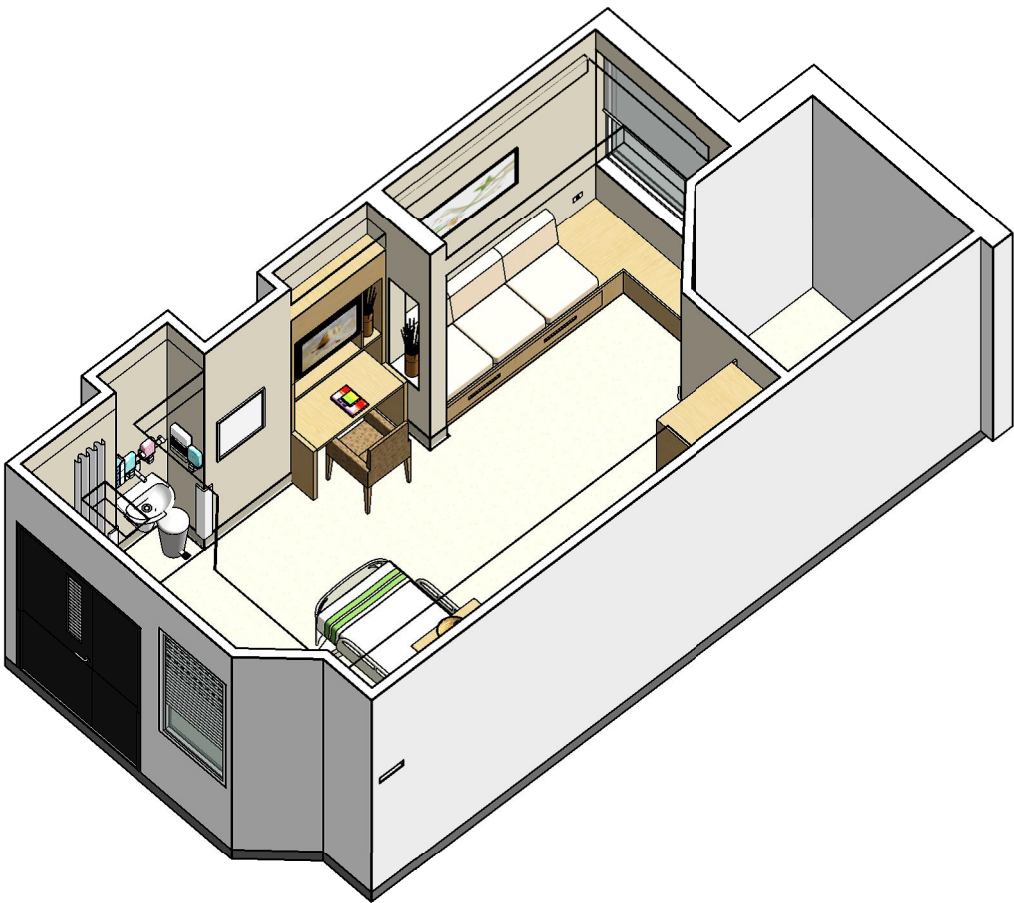

ISOMETRIC VIEW 02

REV	DESCRIPTION	DATE	BY	REV	DESCRIPTION	DATE	BY	REV	DESCRIPTION	DATE	BY
1	FIRST REVISION	22.02.2013	CT								
2	SECOND REVISION	30.05.2013	NB								

iHFG

International Health Facility Guidelines

International Health Facility Guidelines at:
www.healthdesign.com.au/iHFG
Editable version of Standard Components on
Health Facility Briefing System (HFBS) at:
www.healthdesign.com.au
©TAHPI

DESIGNED	APPROVED	DATE	SCALE(S)	SHEET
RC/ CT/ NB	DB	02/19/13		4 of 5
REVIT FILE NAME	PAPER DRAWING ID	ISSUE		
1 BR-LG-28B-I	1 BR-LG-28B-Ie	1		

This document is for advisory purpose only

iHFG Standard Components

Room Layout Sheet

Room Name | 1 Bed Room - Large, 28m²

RLS Room Code 1 BR-LG-28B-I
RDS Room Code 1 BR-LG-28B-I



PERSPECTIVE 01 NEW



PERSPECTIVE 02



PERSPECTIVE 03

REV	DESCRIPTION	DATE	BY	REV	DESCRIPTION	DATE	BY	REV	DESCRIPTION	DATE	BY
1	FIRST REVISION	22.02.2013	CT								
2	SECOND REVISION	30.05.2013	NB								

	International Health Facility Guidelines	International Health Facility Guidelines at: www.healthdesign.com.au/iHfg Editable version of Standard Components on Health Facility Briefing System (HFBS) at: www.healthdesign.com.au ©TAHPI	DESIGNED	APPROVED	DATE	SCALE(S)	SHEET
			RC / CT	DB	18/10/12	1 : 1	5 of 5
			REVIT FILE NAME	PAPER DRAWING ID	ISSUE		
1 BR-LG-28B-I	1 BR-LG-28B-I	1					



The International Health Facility Guidelines recommends the use of HFBS “Health Facility Briefing System” to edit all room data sheet information for your project.

HFBS provides edit access to all iHFG standard rooms, and departments, and more than 100 custom report templates.

HFBS Health Facility Briefing System



Briefing Module

The Health Facility Briefing System (HFBS) has numerous modules available via annual subscription. It suits healthcare Architects, Medical Planners, Equipment Planners Project Managers and Health Authorities.

Use the HFBS Briefing Module to quickly drag in health facility departments or pre-configured room templates from the iHFG standard, edit the room features such as finishes, furniture, fittings, fixtures, medical equipment, engineering services. The system can print or download as PDF more than 100 custom reports including room data sheets, schedules, and more...

To learn more about the HFBS web-based Healthcare Briefing and Design Software and to obtain editable versions of the “Standard Components” including Room Data Sheets (RDS) and Room Layout Sheets (RLS) offered on the iHFG website, signup for HFBS using the link below.

Get Started Now:
hfbs.healthdesign.com.au

- ✓ iHFG Room Data Sheets and Departments are instantly editable in the HFBS software available online.
- ✓ You can access hundreds of report templates to print your iHFG room data in HFBS.
- ✓ HFBS has a onetime free 3 day trial available to all new users.

Get Started Now:
hfbs.healthdesign.com.au



HFBS

Health Facility Briefing System

hfbsinfo.com | techsupport@healthdesign.com.au